



Changement de destination de logements en bureaux

Permis de construire

Date : 06/03/2026

Nomenclatures des révisions

N° D'INDICE	Date	Description
A	06/03/2026	Changement de destination de logements en bureaux


Maîtrise d'oeuvre

COLLIN
AGATHE


Projet

1 Allée Jean Griffon, 31400, TOULOUSE

Préfixe **837**
Section **AW**
Parcelle **25**
Surface **29 563 m²**

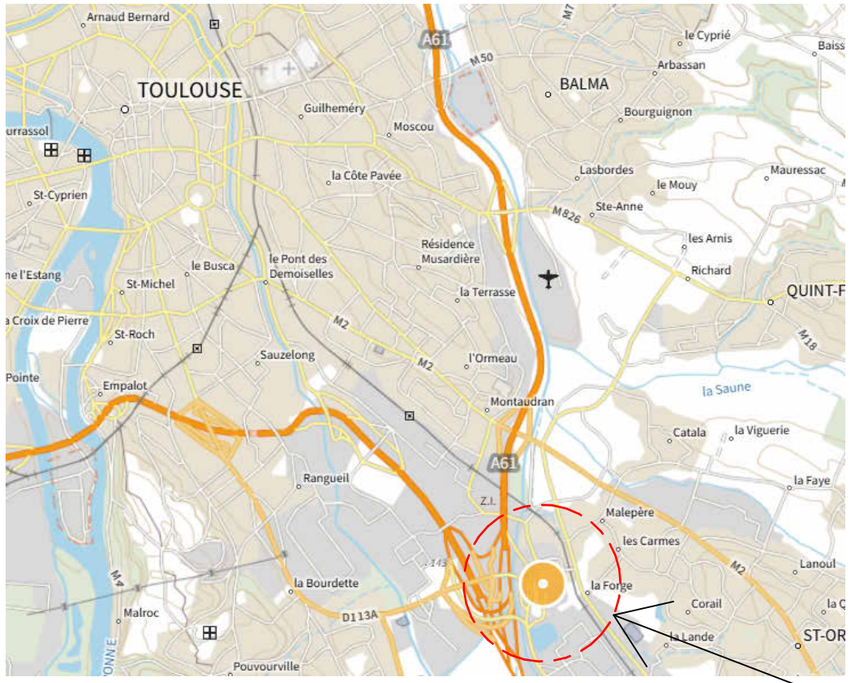

ÉCHELLE MÉTROPOLE

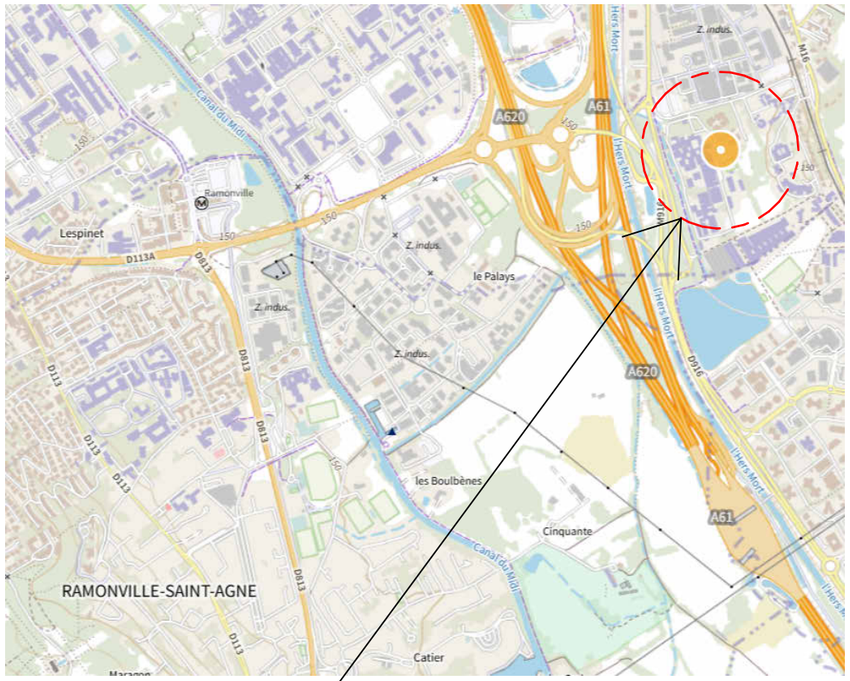

ÉCHELLE VILLE

ÉCHELLE RUE

PROJET

1 Allée Jean Griffon,
31400, TOULOUSE

Préfixe **837**
Section **AW**
Parcelle **25**
Surface **29 563 m²**

N
O
E
S

Bat_AFPA

FEDERATION COMPAGNONNIQUE

A.COLLIN

Ech :

Nomenclature des révisions


N°INDICE	Date	Description

05/03/2026

PERMIS DE CONSTRUIRE

PC 01

Situation

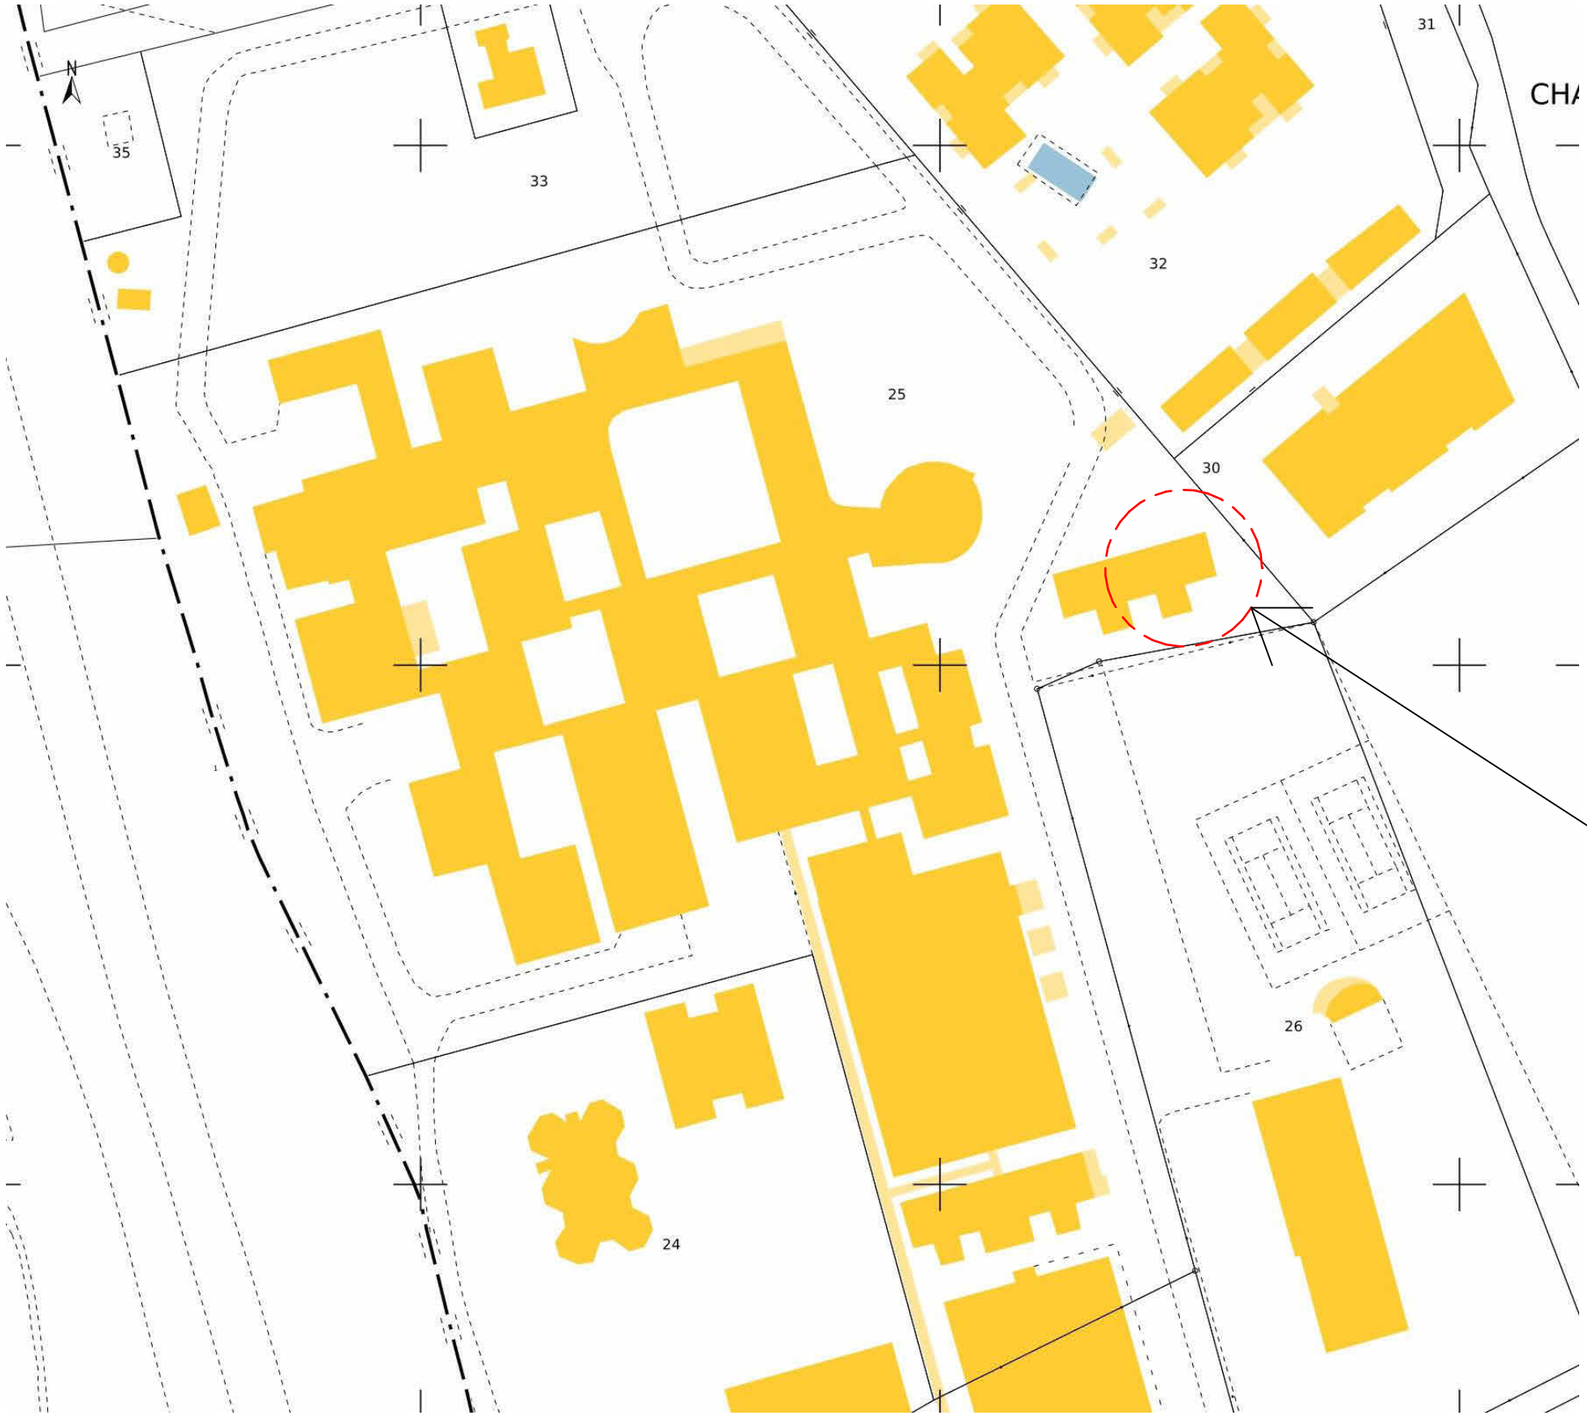

PROJET

1 Allée Jean Griffon,
31400, TOULOUSE

Préfixe **837**
Section **AW**
Parcelle **25**
Surface **29 563 m²**



Bat_AFPA

FEDERATION COMPAGNONNIQUE

A.COLLIN

Ech :


Nomenclature des révisions		
N°INDICE	Date	Description

05/03/2026

PERMIS DE CONSTRUIRE

PC 01-2

Cadastre

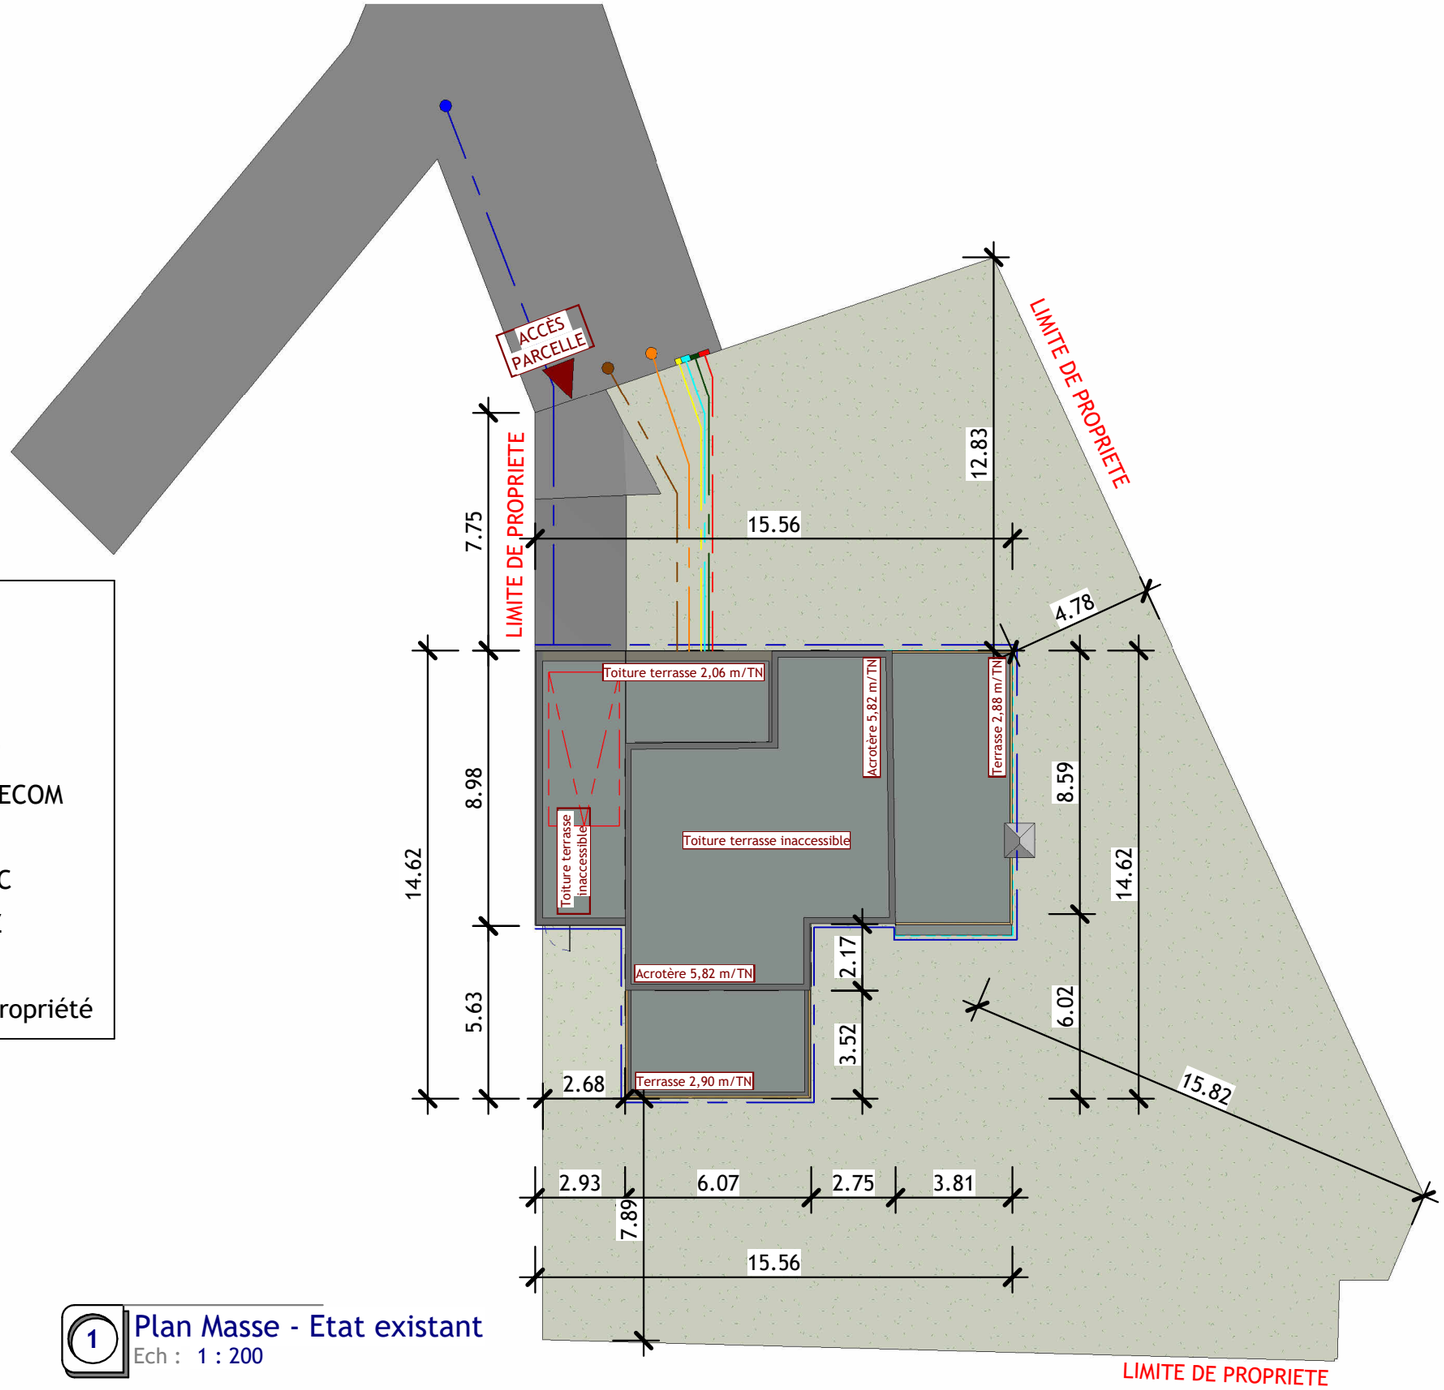

Légende :

- Réseau EU
- Réseau EV
- Réseau AEP
- Réseau TELECOM
- Réseau EP
- Réseau ELEC
- Réseau GAZ
- Limite de propriété

1 Plan Masse - Etat existant
Ech : 1 : 200

Bat_AFPA

FEDERATION COMPAGNONNIQUE

A.COLLIN

Ech : 1 : 200

05/03/2026


PERMIS DE CONSTRUIRE

PC 02

Plan de masse - Etat existant

Nomenclature des révisions

N°INDICE	Date	Description

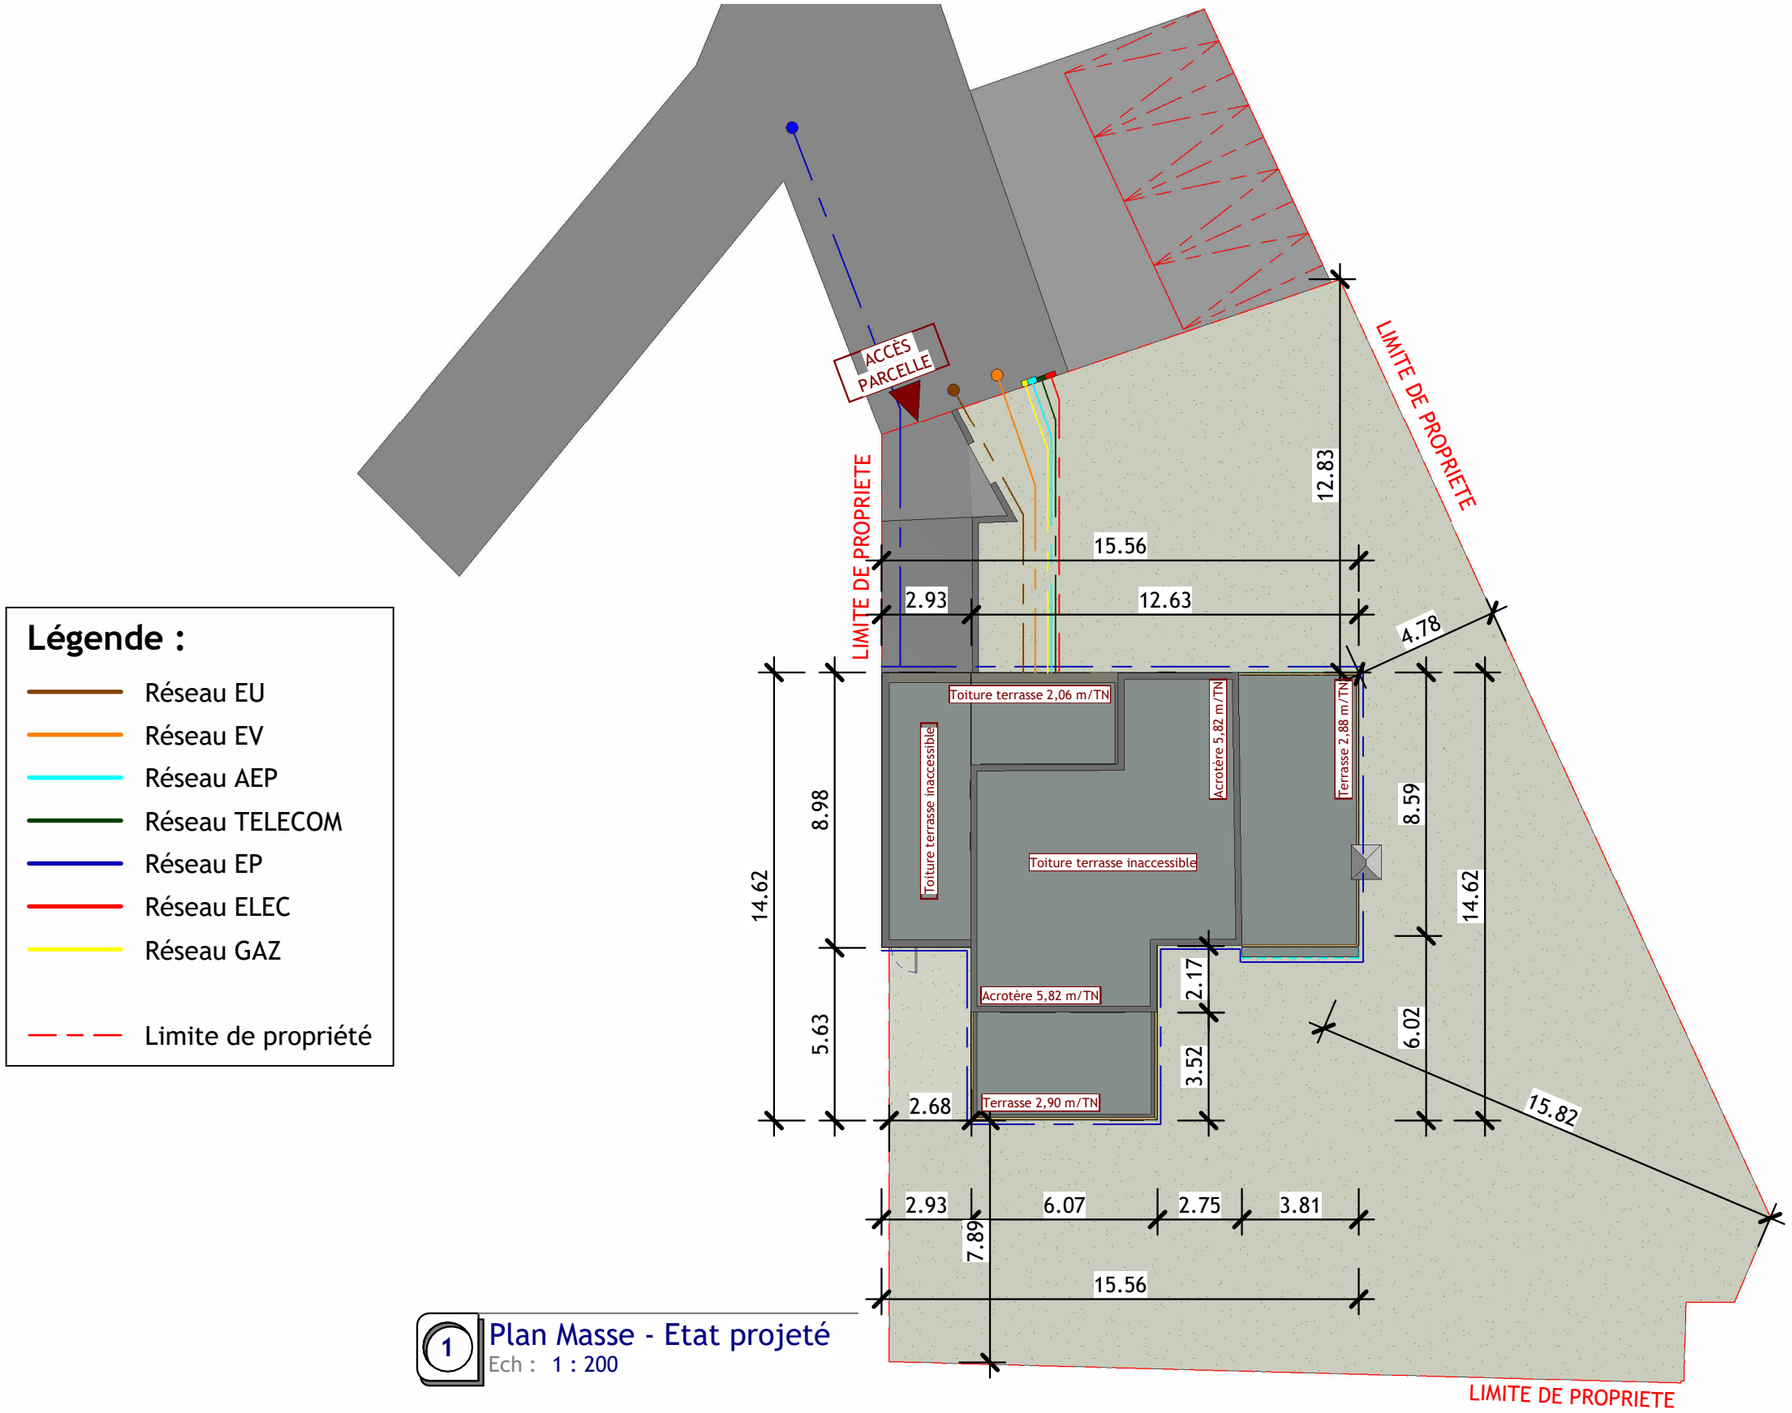


Légende :


- Réseau EU
- Réseau EV
- Réseau AEP
- Réseau TELECOM
- Réseau EP
- Réseau ELEC
- Réseau GAZ
- Limite de propriété

1 Plan Masse - Etat projeté
Ech : 1 : 200

Bat_AFPA FEDERATION COMPAGNONNIQUE	A.COLLIN Ech : 1 : 200	Nomenclature des révisions N°INDICE | Date | Description
05/03/2026 PERMIS DE CONSTRUIRE PC 02-1	Plan de masse - Etat projeté	

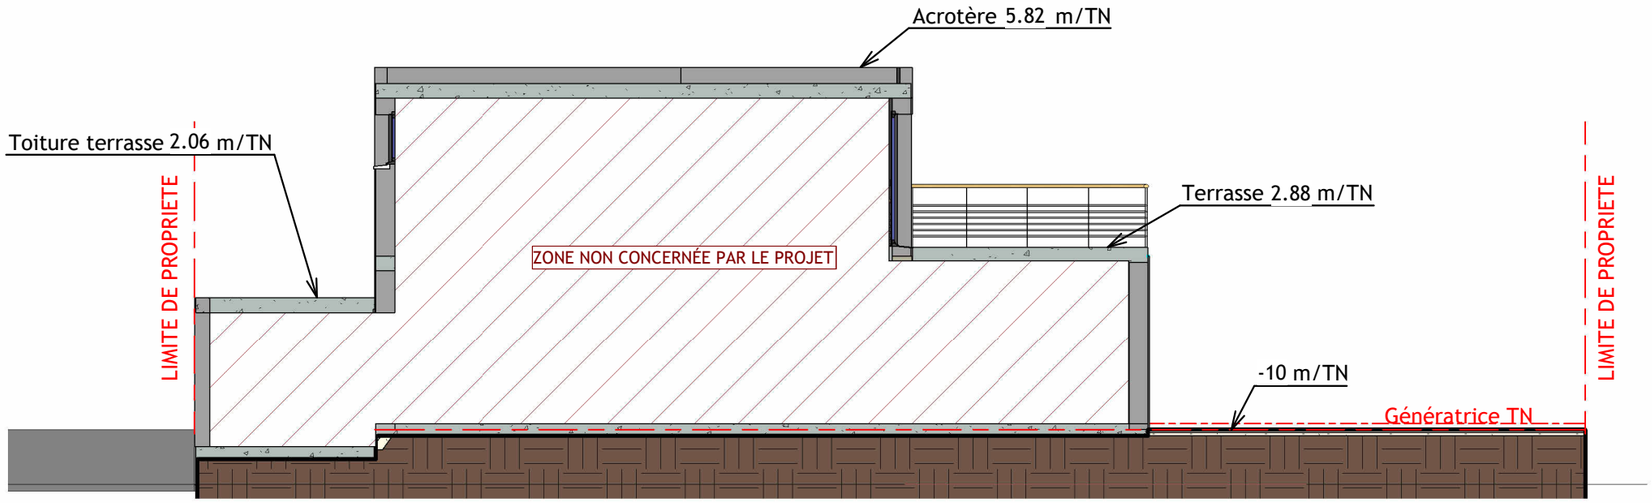

1 Coupe transversale - Etat existant
Ech : 1 : 100

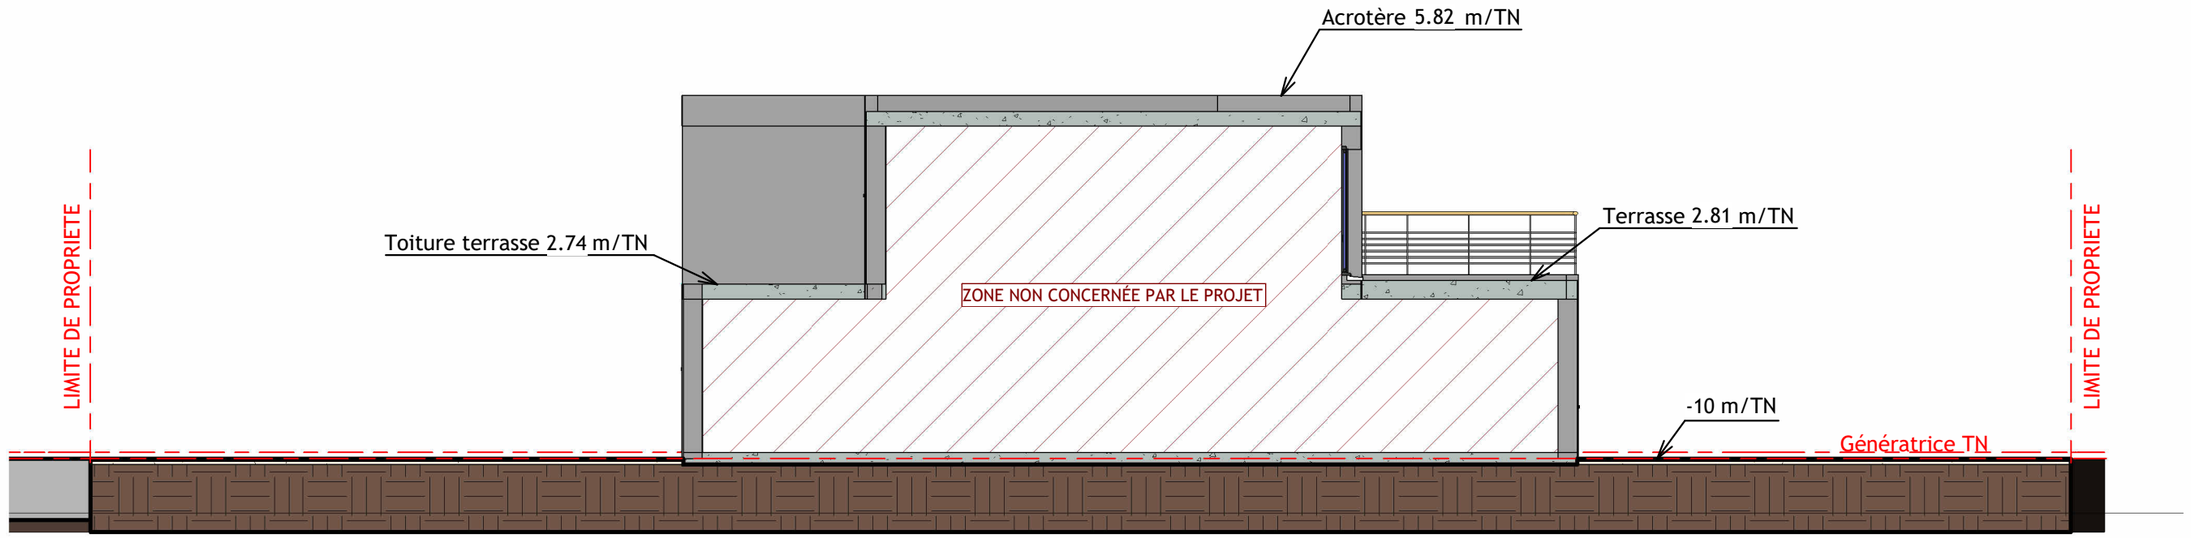

2 Coupe longitudinale - Etat existant
1 : 100

Bat_AFPA

FEDERATION COMPAGNONNIQUE

A.COLLIN

Ech : 1 : 100


Nomenclature des révisions		
N°INDICE	Date	Description

05/03/2026

PERMIS DE CONSTRUIRE


PC 03

Coupes - Etat existant

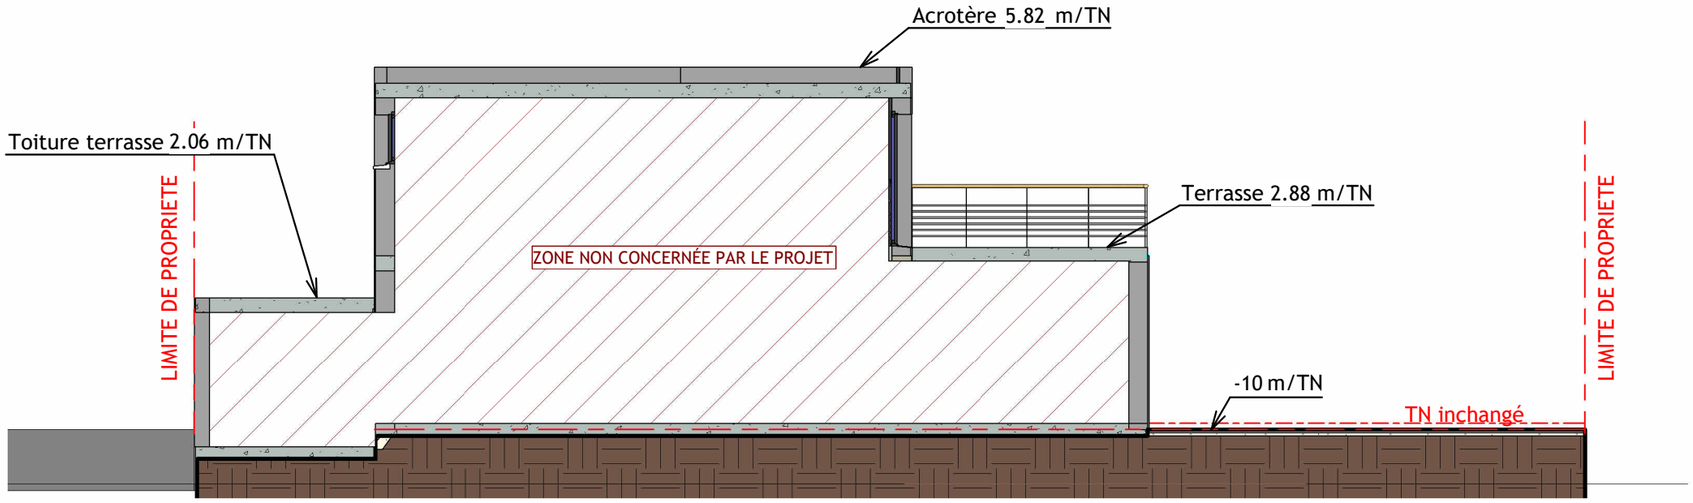

2 Coupe transversale - Etat projeté

Ech : 1 : 100

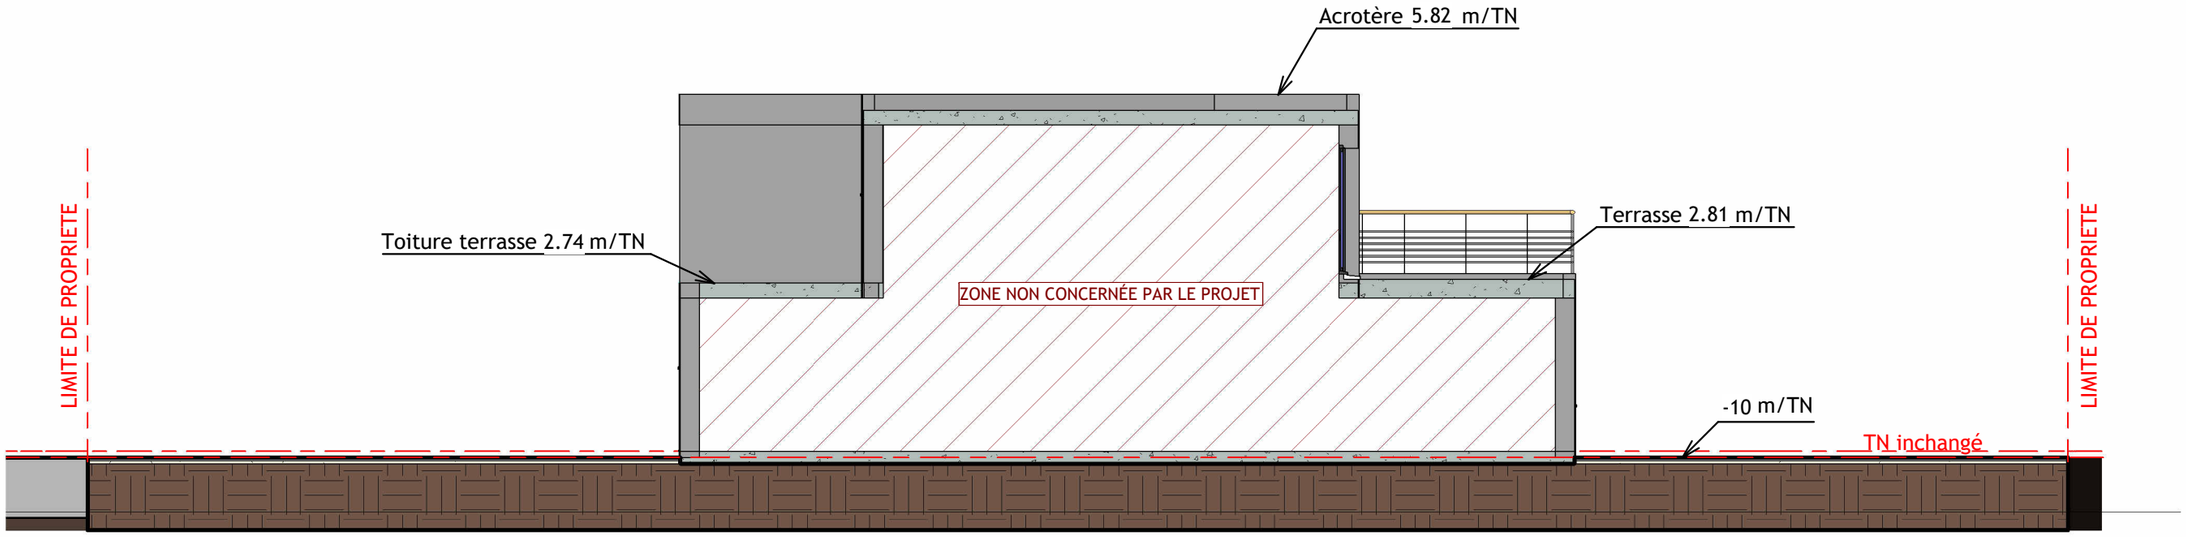

1 Coupe longitudinale - Etat projeté

1 : 100

Bat_AFPA

FEDERATION COMPAGNONNIQUE

A.COLLIN

Ech : 1 : 100

05/03/2026

PERMIS DE CONSTRUIRE

PC 03-1

Coupes - Etat projeté

Nomenclature des révisions

N°INDICE	Date	Description

PC4 -NOTICE DESCRIPTIVE

Projet : Changement de destination de logements en bureaux
1 Allée Jean Griffon, 31400 Toulouse

MOTIVATION DU PROJET
Le maître d'ouvrage est propriétaire d'une unité foncière bâtie sur la commune de Toulouse, il souhaite réaliser un changement de destination de logements en bureaux.

LE SITE
Le lieu. Le programme est situé au 1 Allée Jean Griffon, sur la commune de Toulouse 31400.
L'identité cadastrale de l'unité foncière est section « 837 AW » parcelles N° 25, pour une superficie de 29 563 m².

La morphologie parcellaire et acquis bâti:

Le terrain est de morphologie polygonale régulier, avec +/- 33. mètres au plus long pour +/- 28 mètres au plus large. Le terrain est en pente de +/-1%, dans la zone concernée.
L'accès actuel à l'unité foncière se fait aujourd'hui par une voie privé desservie par l'Allé Jean Griffon. Il sera conservé dans le cadre du projet.
Les végétaux existants sur site, les sujets de hautes tiges seront conservés et protégés à l'occasion du projet. Quoi qu'il en soit, aux abords du projet, aucun végétal de qualité n'est présent.
Les réseaux concessionnaires existants sont Enédis, France-Télécom, AEP. Ils seront conservés, voir complétés aux besoins de l'opération. Aujourd'hui les ordures ménagères sont enlevées au porte à porte.
L'acquis bâti, actuellement l'unité foncière est bâtie, d'une habitation datant des années 1970, des modifications de façade ont été faites auparavant de la demande. Le bâtiment concerné a un impact actuelle de +/- 14.62 mètres de long, pour +/- 15.56 mètres de large et d'une hauteur à l'acrotère de 5.82 mètres à la plus haute acrotère, au terrain de référence. Volumétrie générale, d'un bâtiment en Rez de chaussée avec 1 étages partiel, avec des toitures terrasses.
L'emprise totale actuelle des bâtiments existants est de xxxm², soit xx% de l'unité foncière.
Les façades actuelles sont faites de briquettes en terre cuite, ponctuellement enduites à la chaux teinte gris clair.

L'environnement :
Ce site est dans une zone activité de la commune.



LE PROJET
Le programme - Ce projet a pour but le changement de destination de logements en bureaux ainsi qu'une homogénéisation des façades.

Les implantations et la volumétrie :
Les implantations et le plan de masse, le volume du bâtiment sera inchangé, seul l'intérieur et les façades sont concernées. L'emprise n'est pas affectée et restera inchangée.
La typo-morphologie du bâtiment, la morphologie du bâtiment est « calquée » sur la destination et l'utilisation des locaux afin de favoriser une utilisation optimale des surfaces et une reconnaissance des bâtiments suivant leur fonction.
Toutes les façades seront enduites d'un enduit gratté fin teinte gris-beige, ton beige RAL 1014 afin de s'homogénéiser avec la paysage alentour.
Façade Nord : Restitution d'une menuiserie supprimée auparavant. Modification d'une menuiserie (porte de garage) remplacée par une fenêtre en PVC teinte 7016 idem menuiseries existantes

LES ABORDS DU PROJET
La clôture, inchangée au projet
Les espaces verts, abords et accès, non modifiés au projet
Les ordures ménagères, Sans objet, pour le présent projet
Les réseaux divers - Aujourd'hui l'ensemble des réseaux sont existants et conservés sur site. Ils seront complétés à l'occasion du projet, en fonction des besoins du programme et des avis des services concessionnaires concernés.
Réseau d'eau pluvial collectif.


Analyse des risques

Les risques naturels identifiés dans la zone du projet sont :
- Inondation
- Remontée de nappes
- Mouvements de terrain
- Retrait de gonflement des argiles

Les risques naturels identifiés dans la zone du projet sont :
- Canalisations de transport de matières dangereuses
- Pollution des sols

Ces risques sont bien pris en compte en projet, même si aucunes modifications structurelles majeures sont prévues.

Bat_AFPA FEDERATION COMPAGNONNIQUE		A.COLLIN Ech :	Nomenclature des révisions N°INDICE / Date / Description
05/03/2026 PERMIS DE CONSTRUIRE PC 04	Notice descriptive		

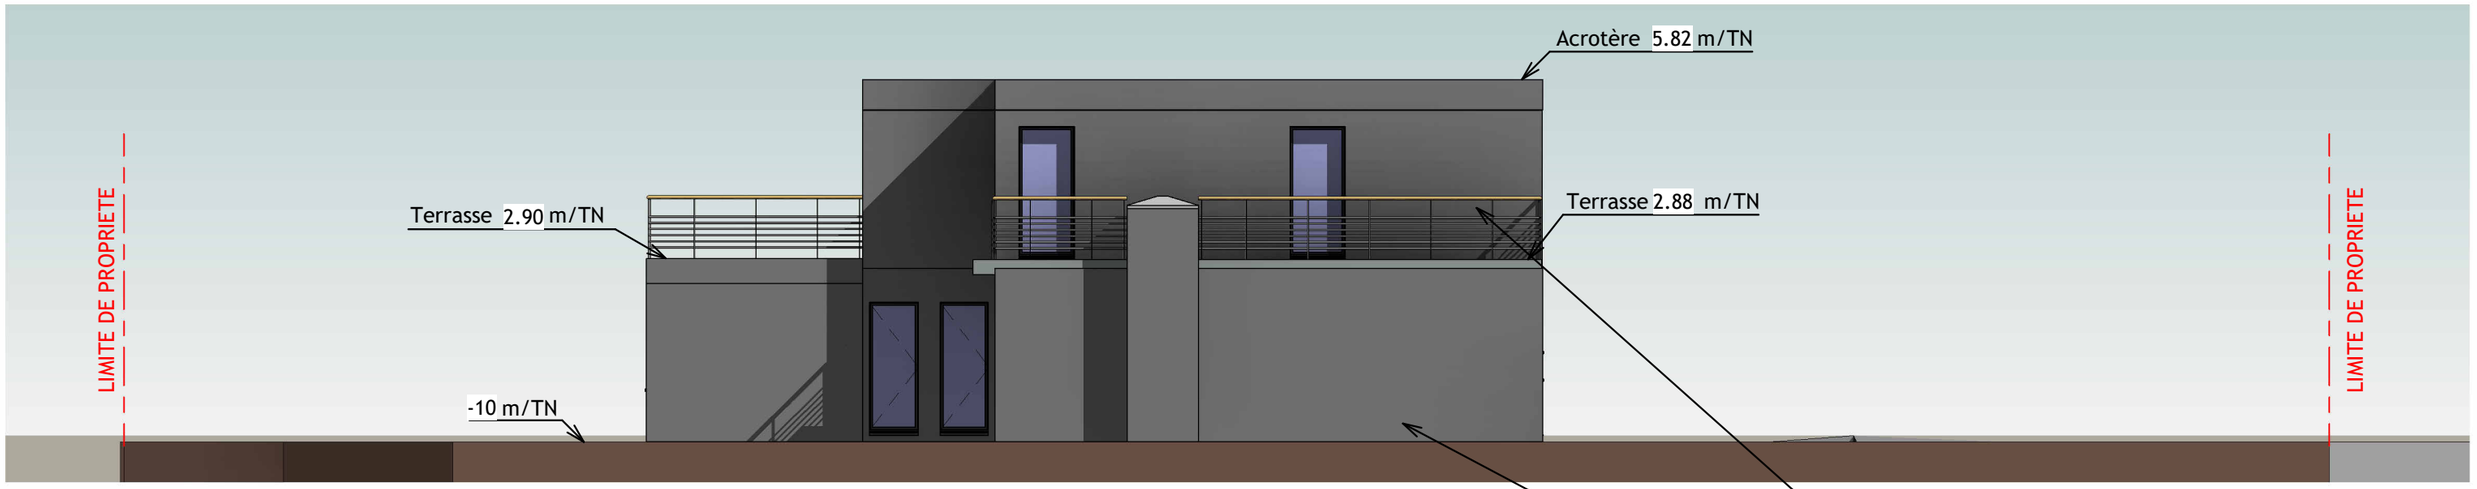


1 Elévation Est - Etat existant
Ech : 1 : 100

Légende

Façade en briquette terre cuite

Menuiseries PVC RAL 7016

Enduit à la chaux teinte gris

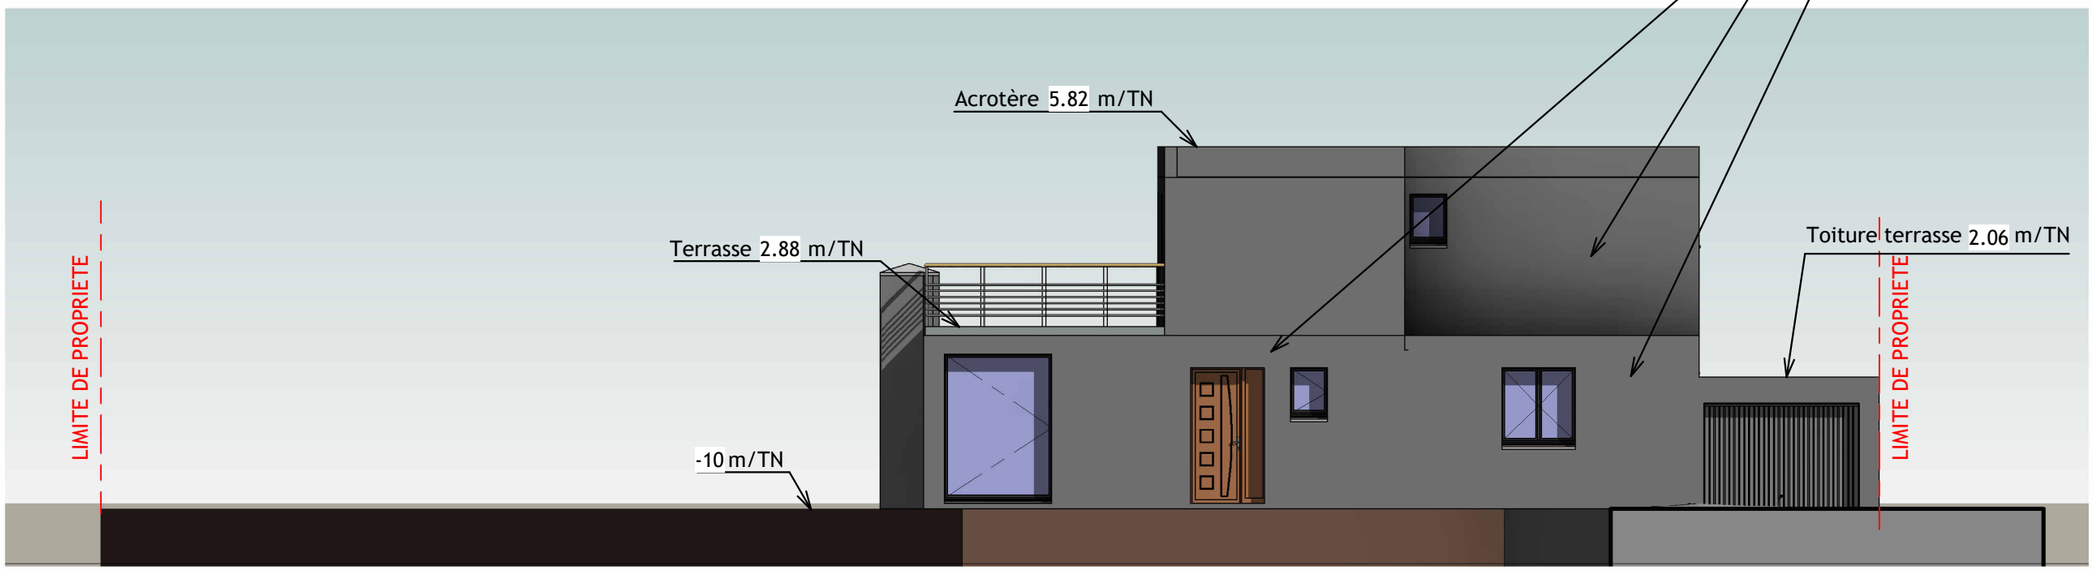

2 Elévation Nord - Etat existant
Ech : 1 : 100

Bat_AFPA

FEDERATION COMPAGNONNIQUE

A.COLLIN

Ech : 1 : 100

05/03/2026

PERMIS DE CONSTRUIRE

PC 05

Façades N/E - Etat existant

Nomenclature des révisions

N°INDICE	Date	Description




1 Elévation Ouest - Etat existant
Ech : 1 : 100

Légende

Façade en briquette terre cuite

Menuiseries PVC RAL 7016

Enduit à la chaux teinte gris

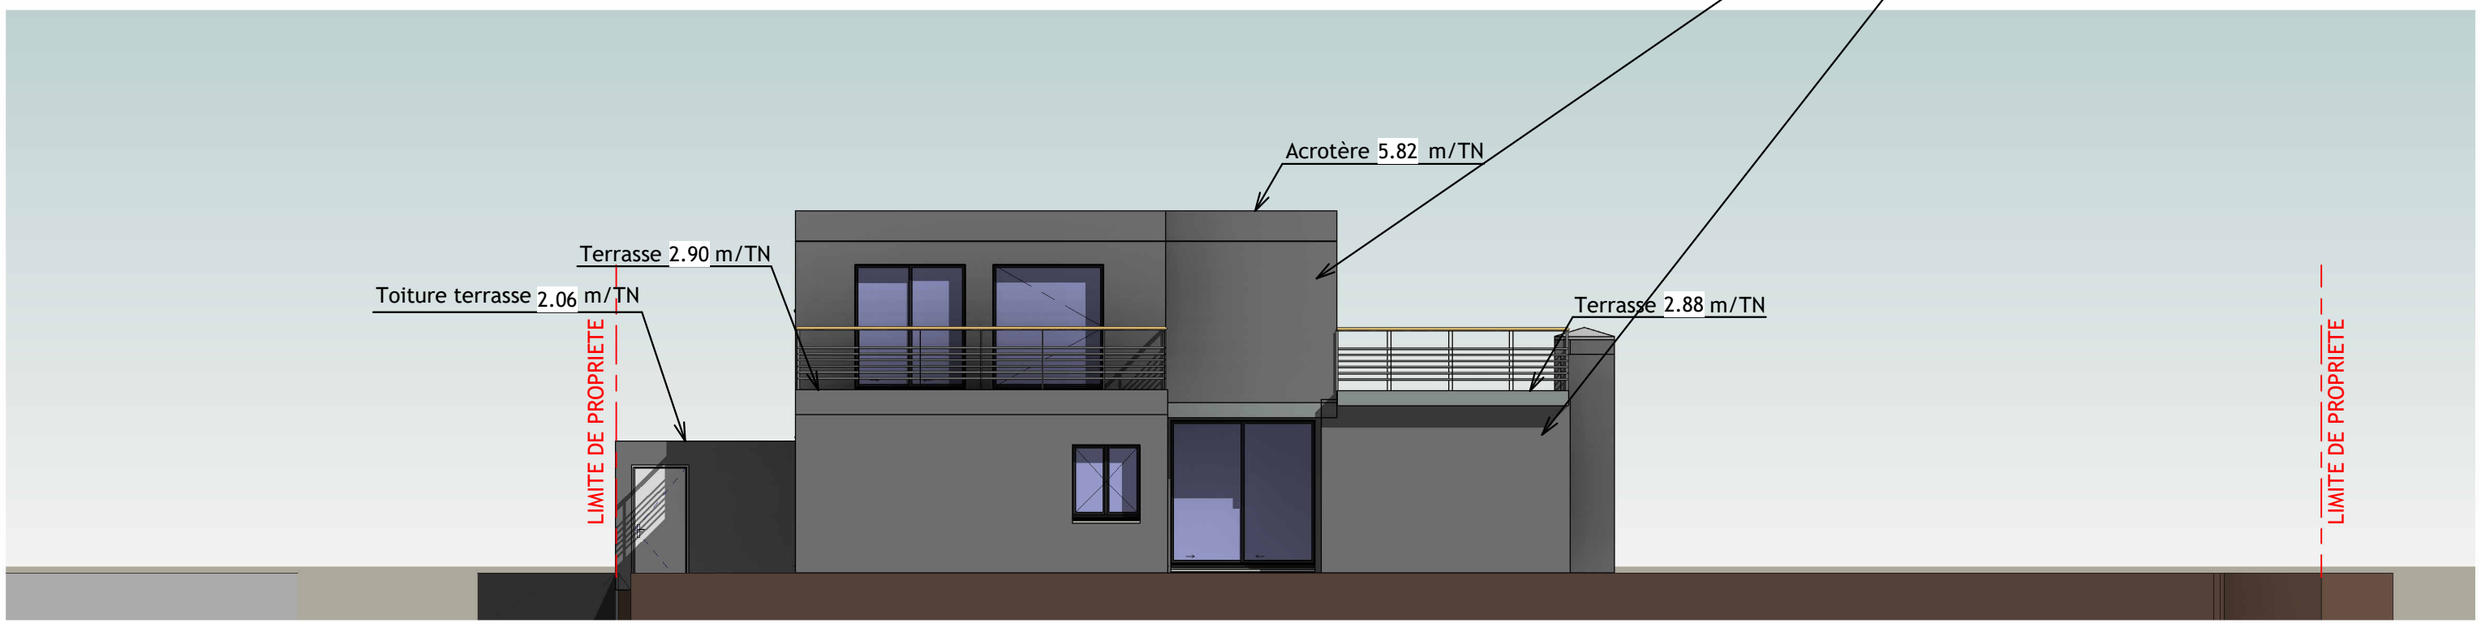

2 Elévation Sud - Etat existant
Ech : 1 : 100

Bat_AFPA

FEDERATION COMPAGNONNIQUE

A.COLLIN

Ech : 1 : 100

05/03/2026


PERMIS DE CONSTRUIRE

PC 05-1

Façades S/O - Etat existant

Nomenclature des révisions

N°INDICE	Date	Description

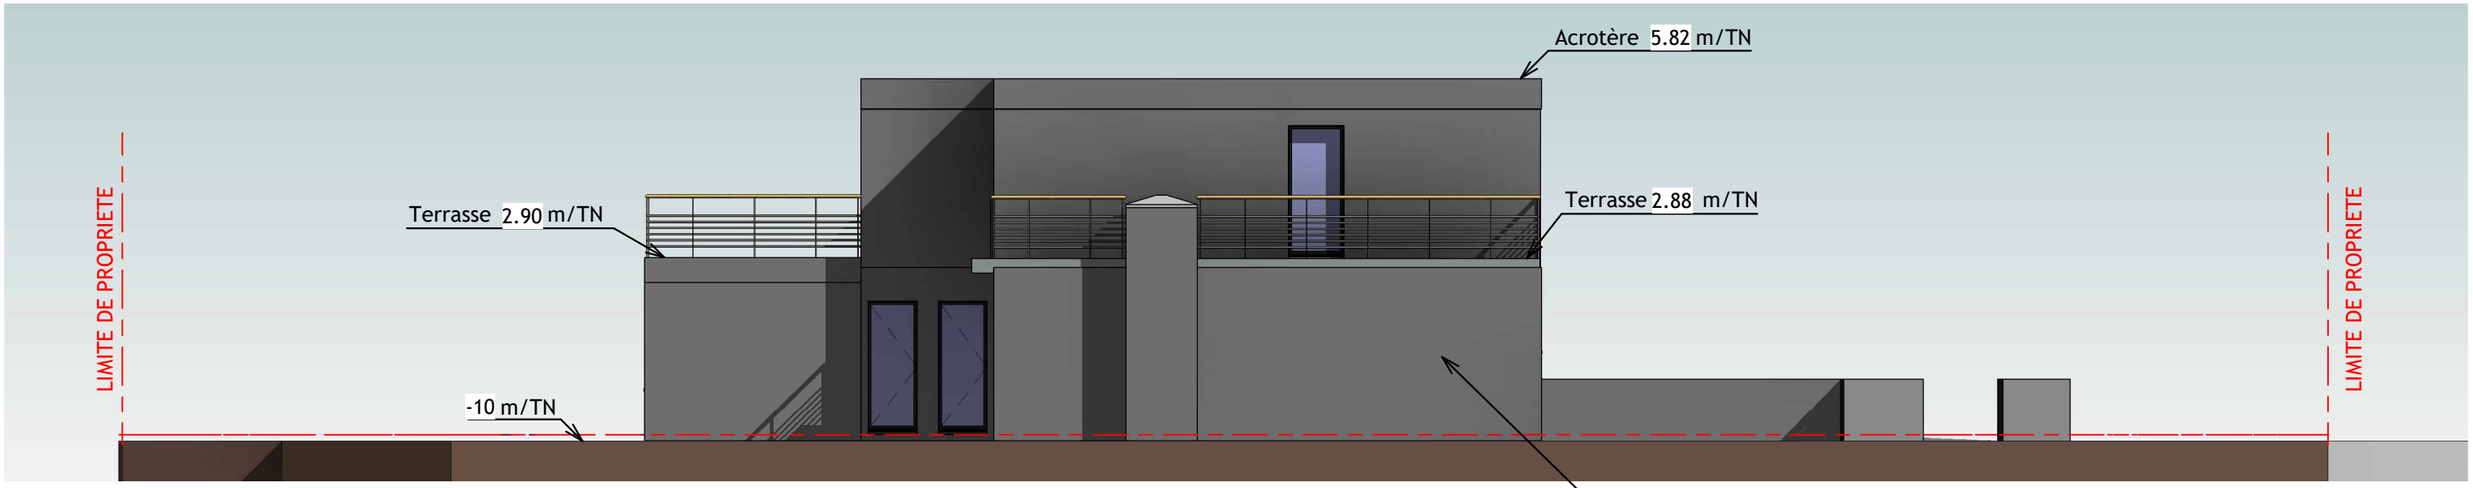


2 Elévation Est - Etat projeté
Ech : 1 : 100

Légende

Enduit gratté fin, teinte beige RAL 1014

Menuiseries PVC RAL 7016

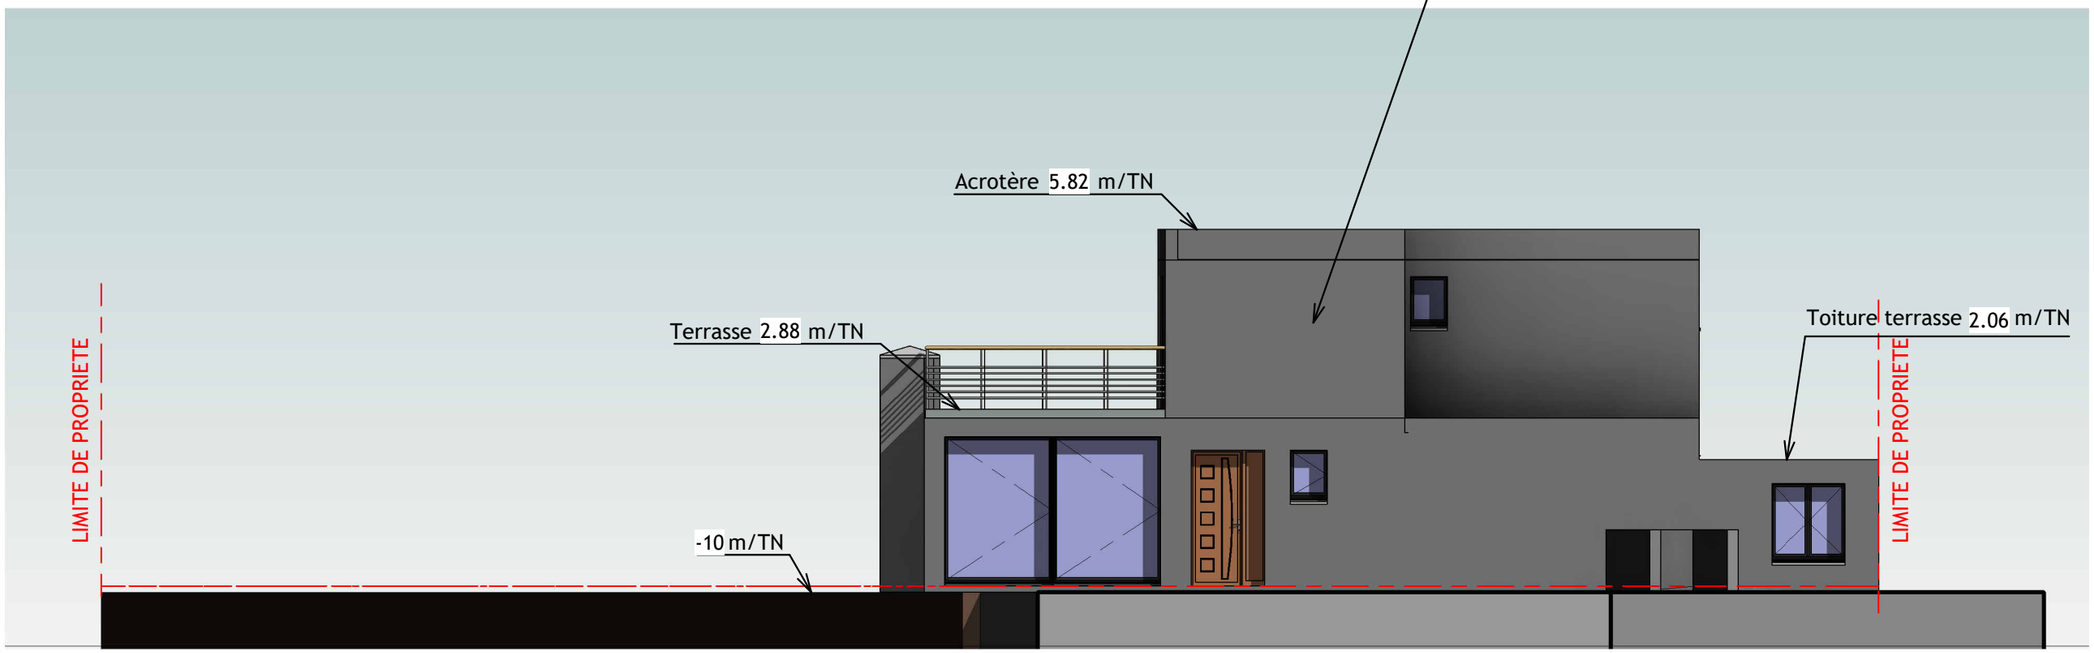

1 Elévation Nord - Etat projeté
Ech : 1 : 100

Bat_AFPA

FEDERATION COMPAGNONNIQUE

A.COLLIN

Ech : 1 : 100

05/03/2026


PERMIS DE CONSTRUIRE

PC 05-2

Façades N/E - Etat projeté

Nomenclature des révisions

N°INDICE	Date	Description

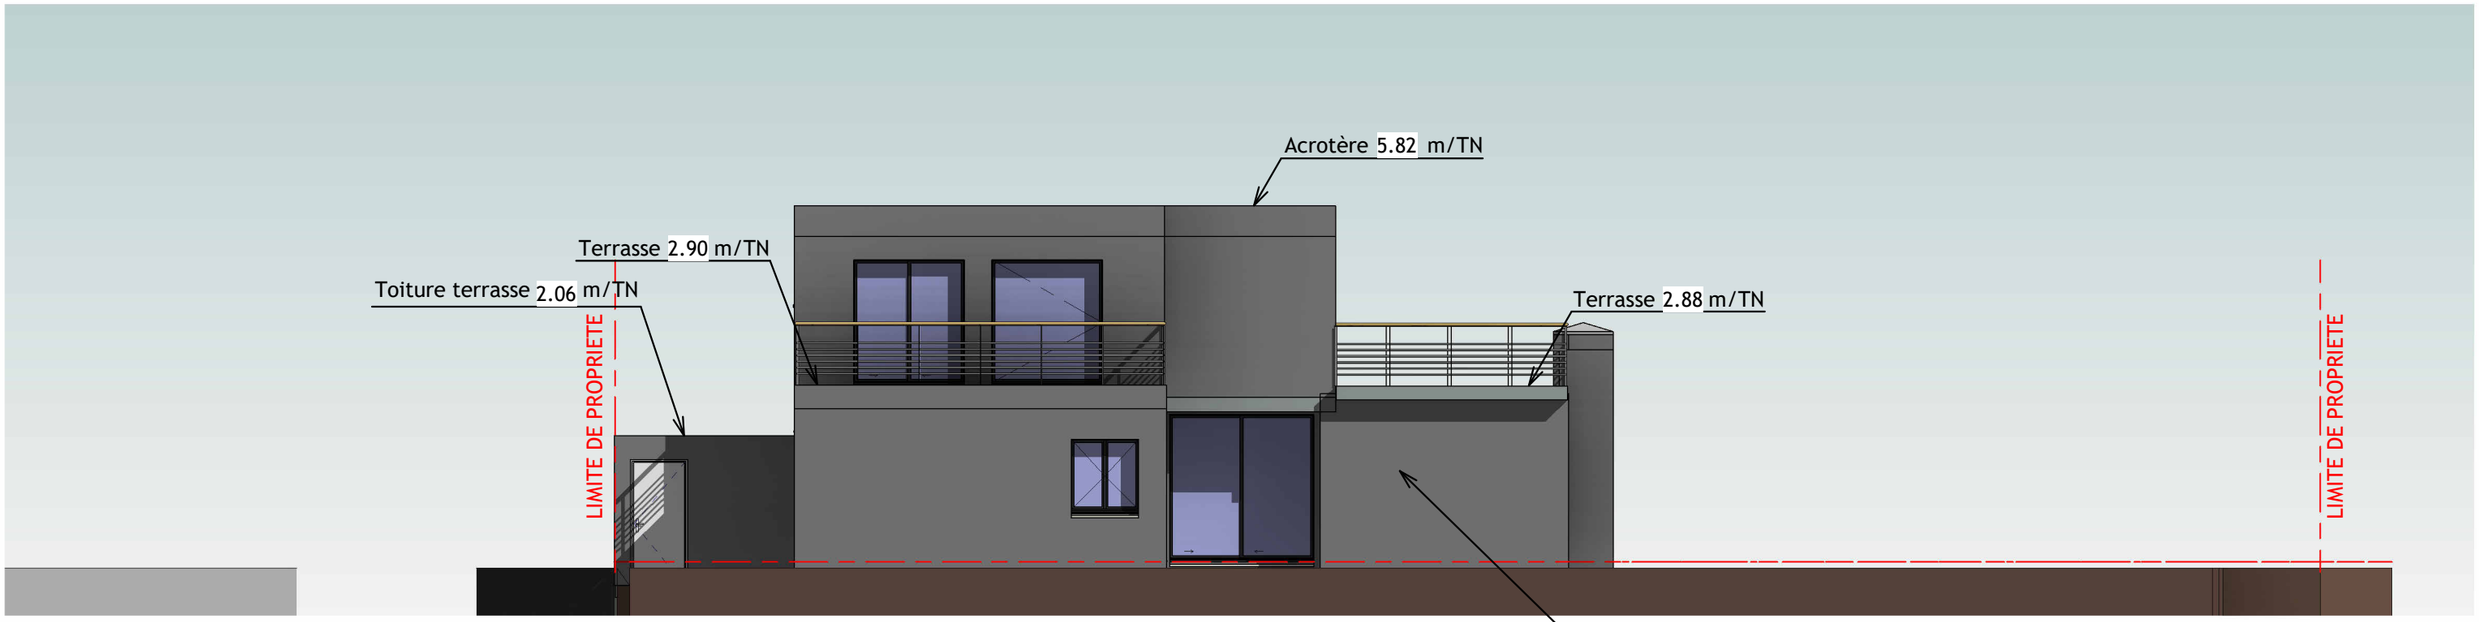


1 Elévation Sud - Etat projeté
Ech : 1 : 100

Légende

Enduit gratté fin, teinte beige RAL 1014

Menuiseries PVC RAL 7016

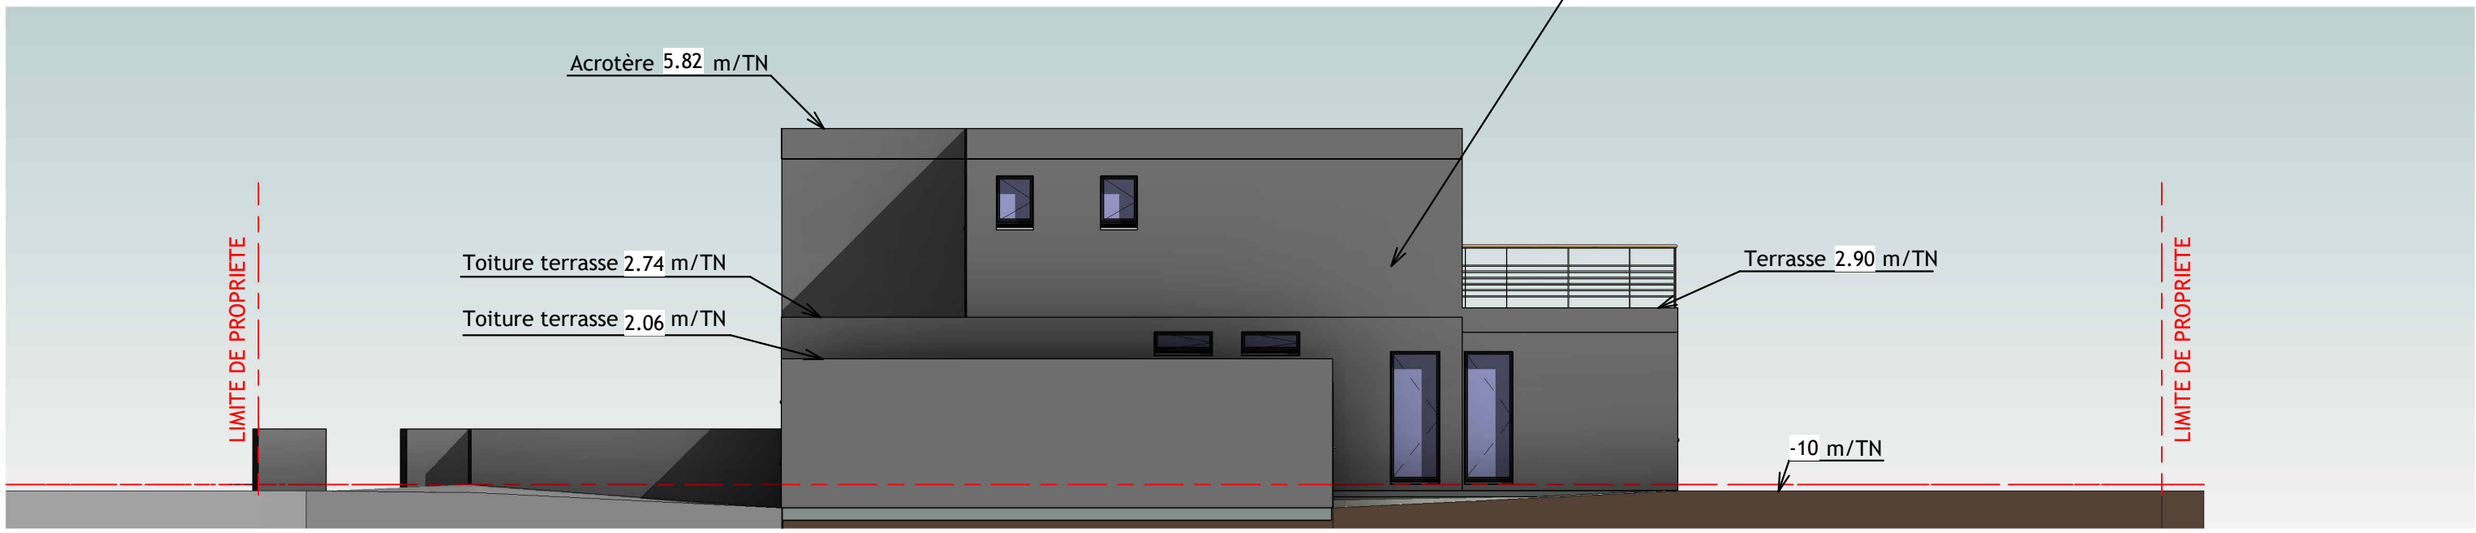

2 Elévation Ouest - Etat projeté
Ech : 1 : 100

Bat_AFPA

FEDERATION COMPAGNONNIQUE

A.COLLIN

Ech : 1 : 100

05/03/2026


PERMIS DE CONSTRUIRE

PC 05-3

Façades S/O - Etat projeté

Nomenclature des révisions

N°INDICE	Date	Description

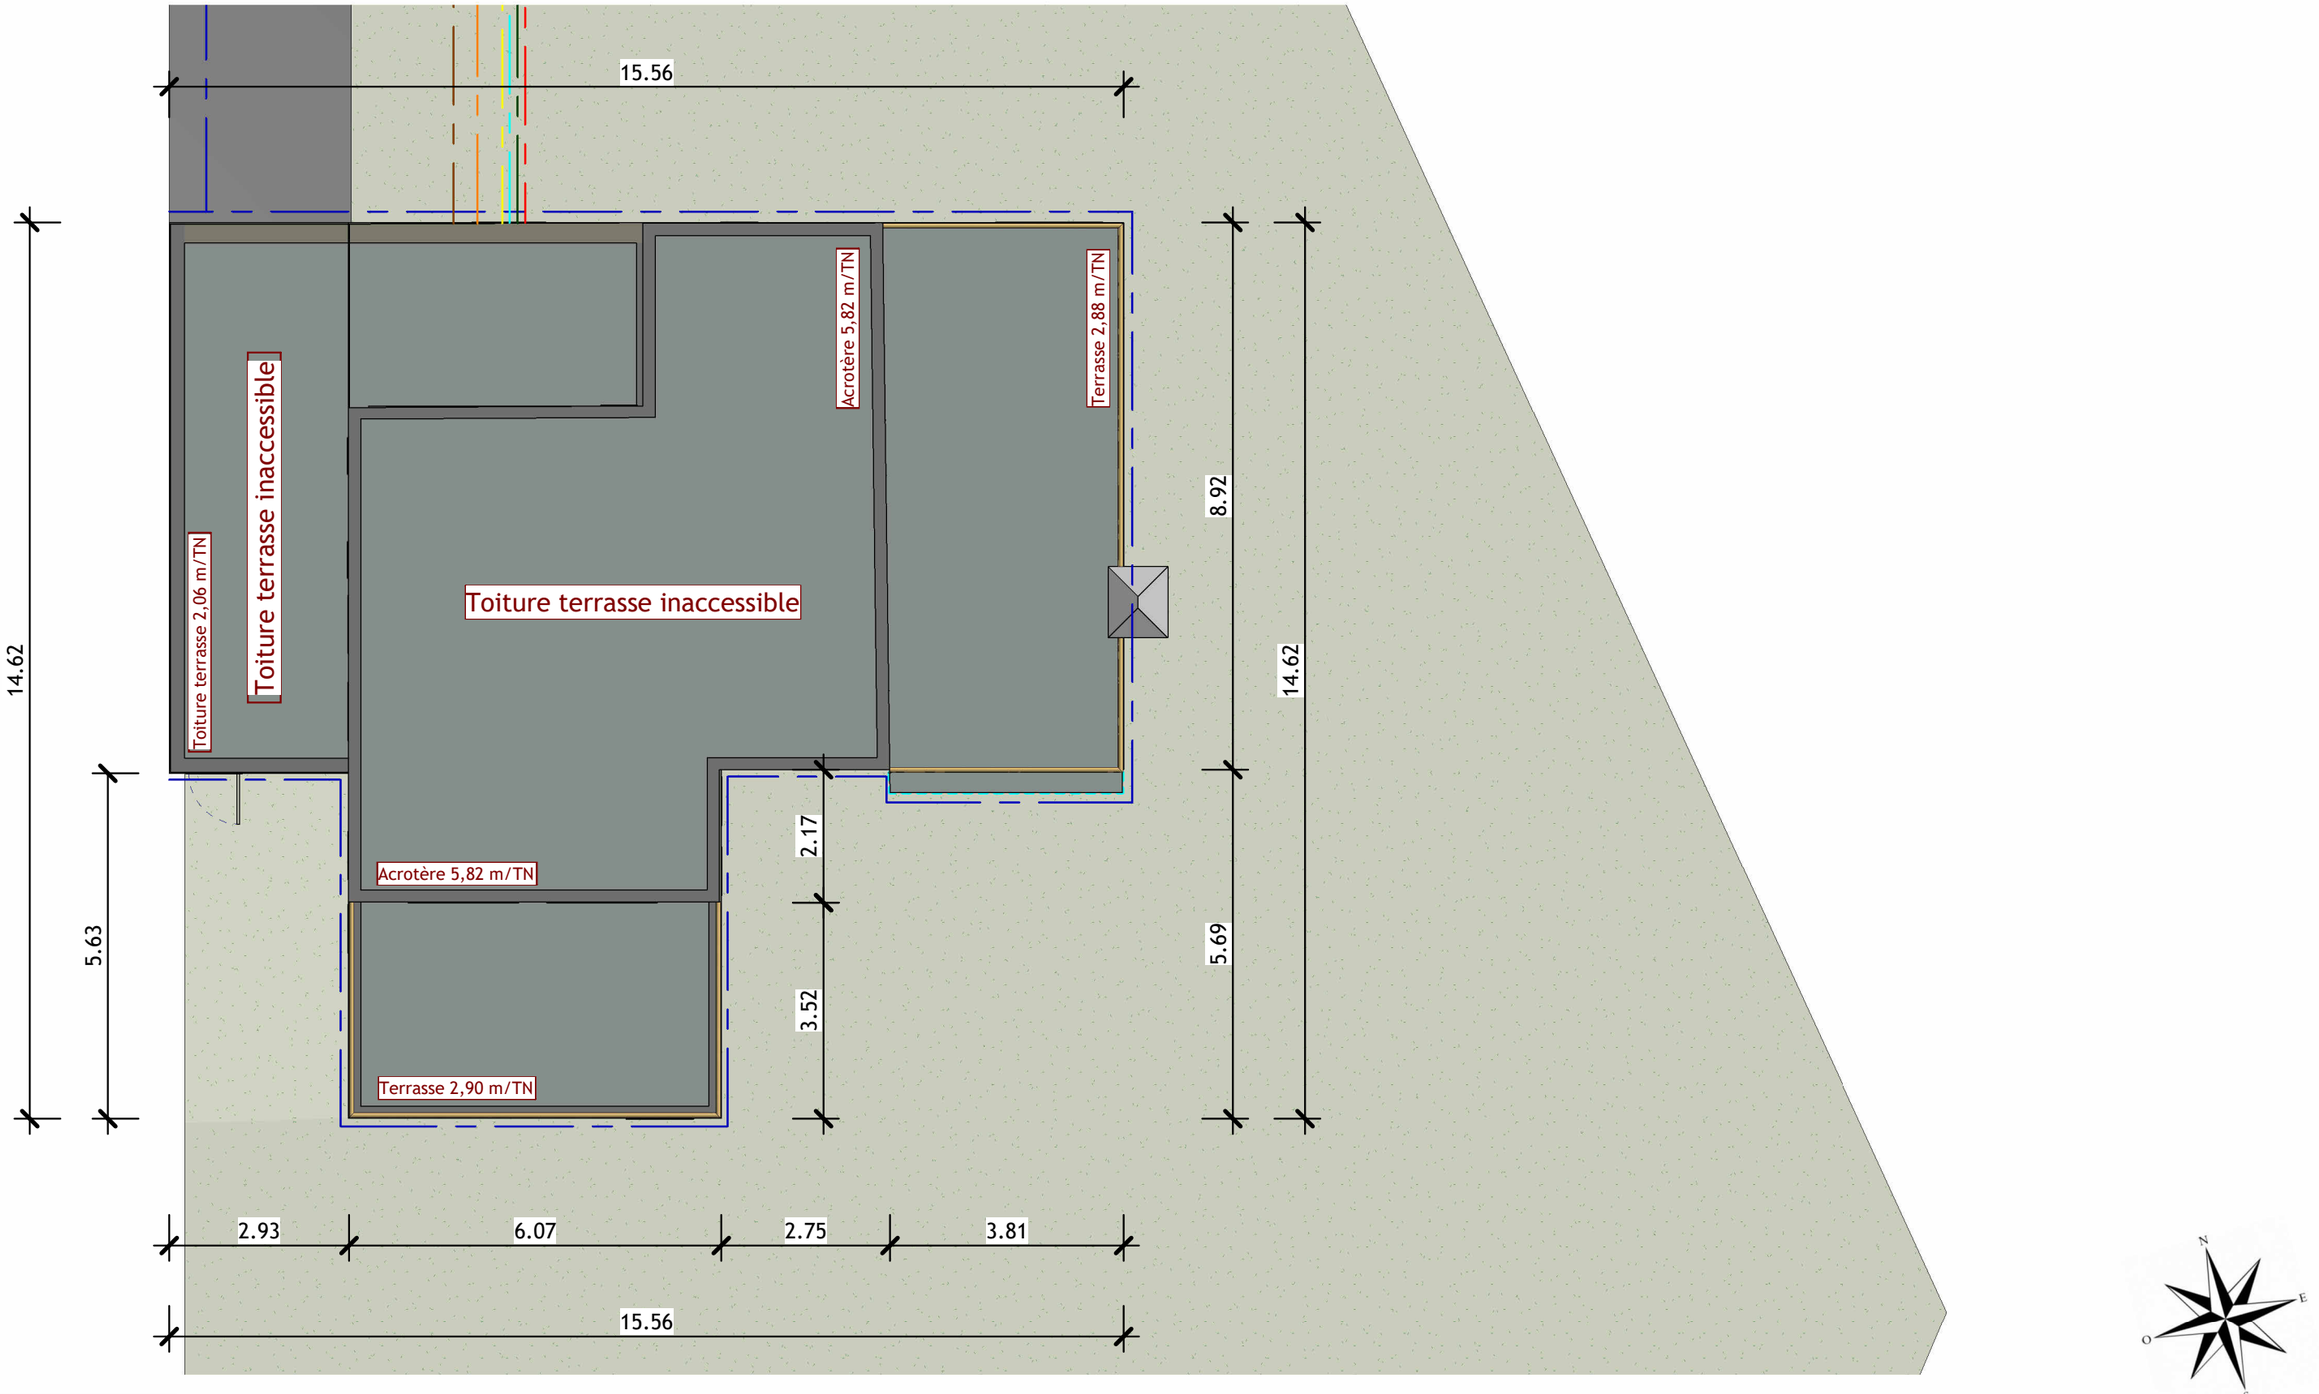

1 Plan de toitures - Etat existant
Ech : 1 : 100

Bat_AFPA

FEDERATION COMPAGNONNIQUE

A.COLLIN

Ech : 1 : 100

05/03/2026


PERMIS DE CONSTRUIRE

PC 05-4

Plan de toiture - Etat existant

Nomenclature des révisions

N°INDICE	Date	Description

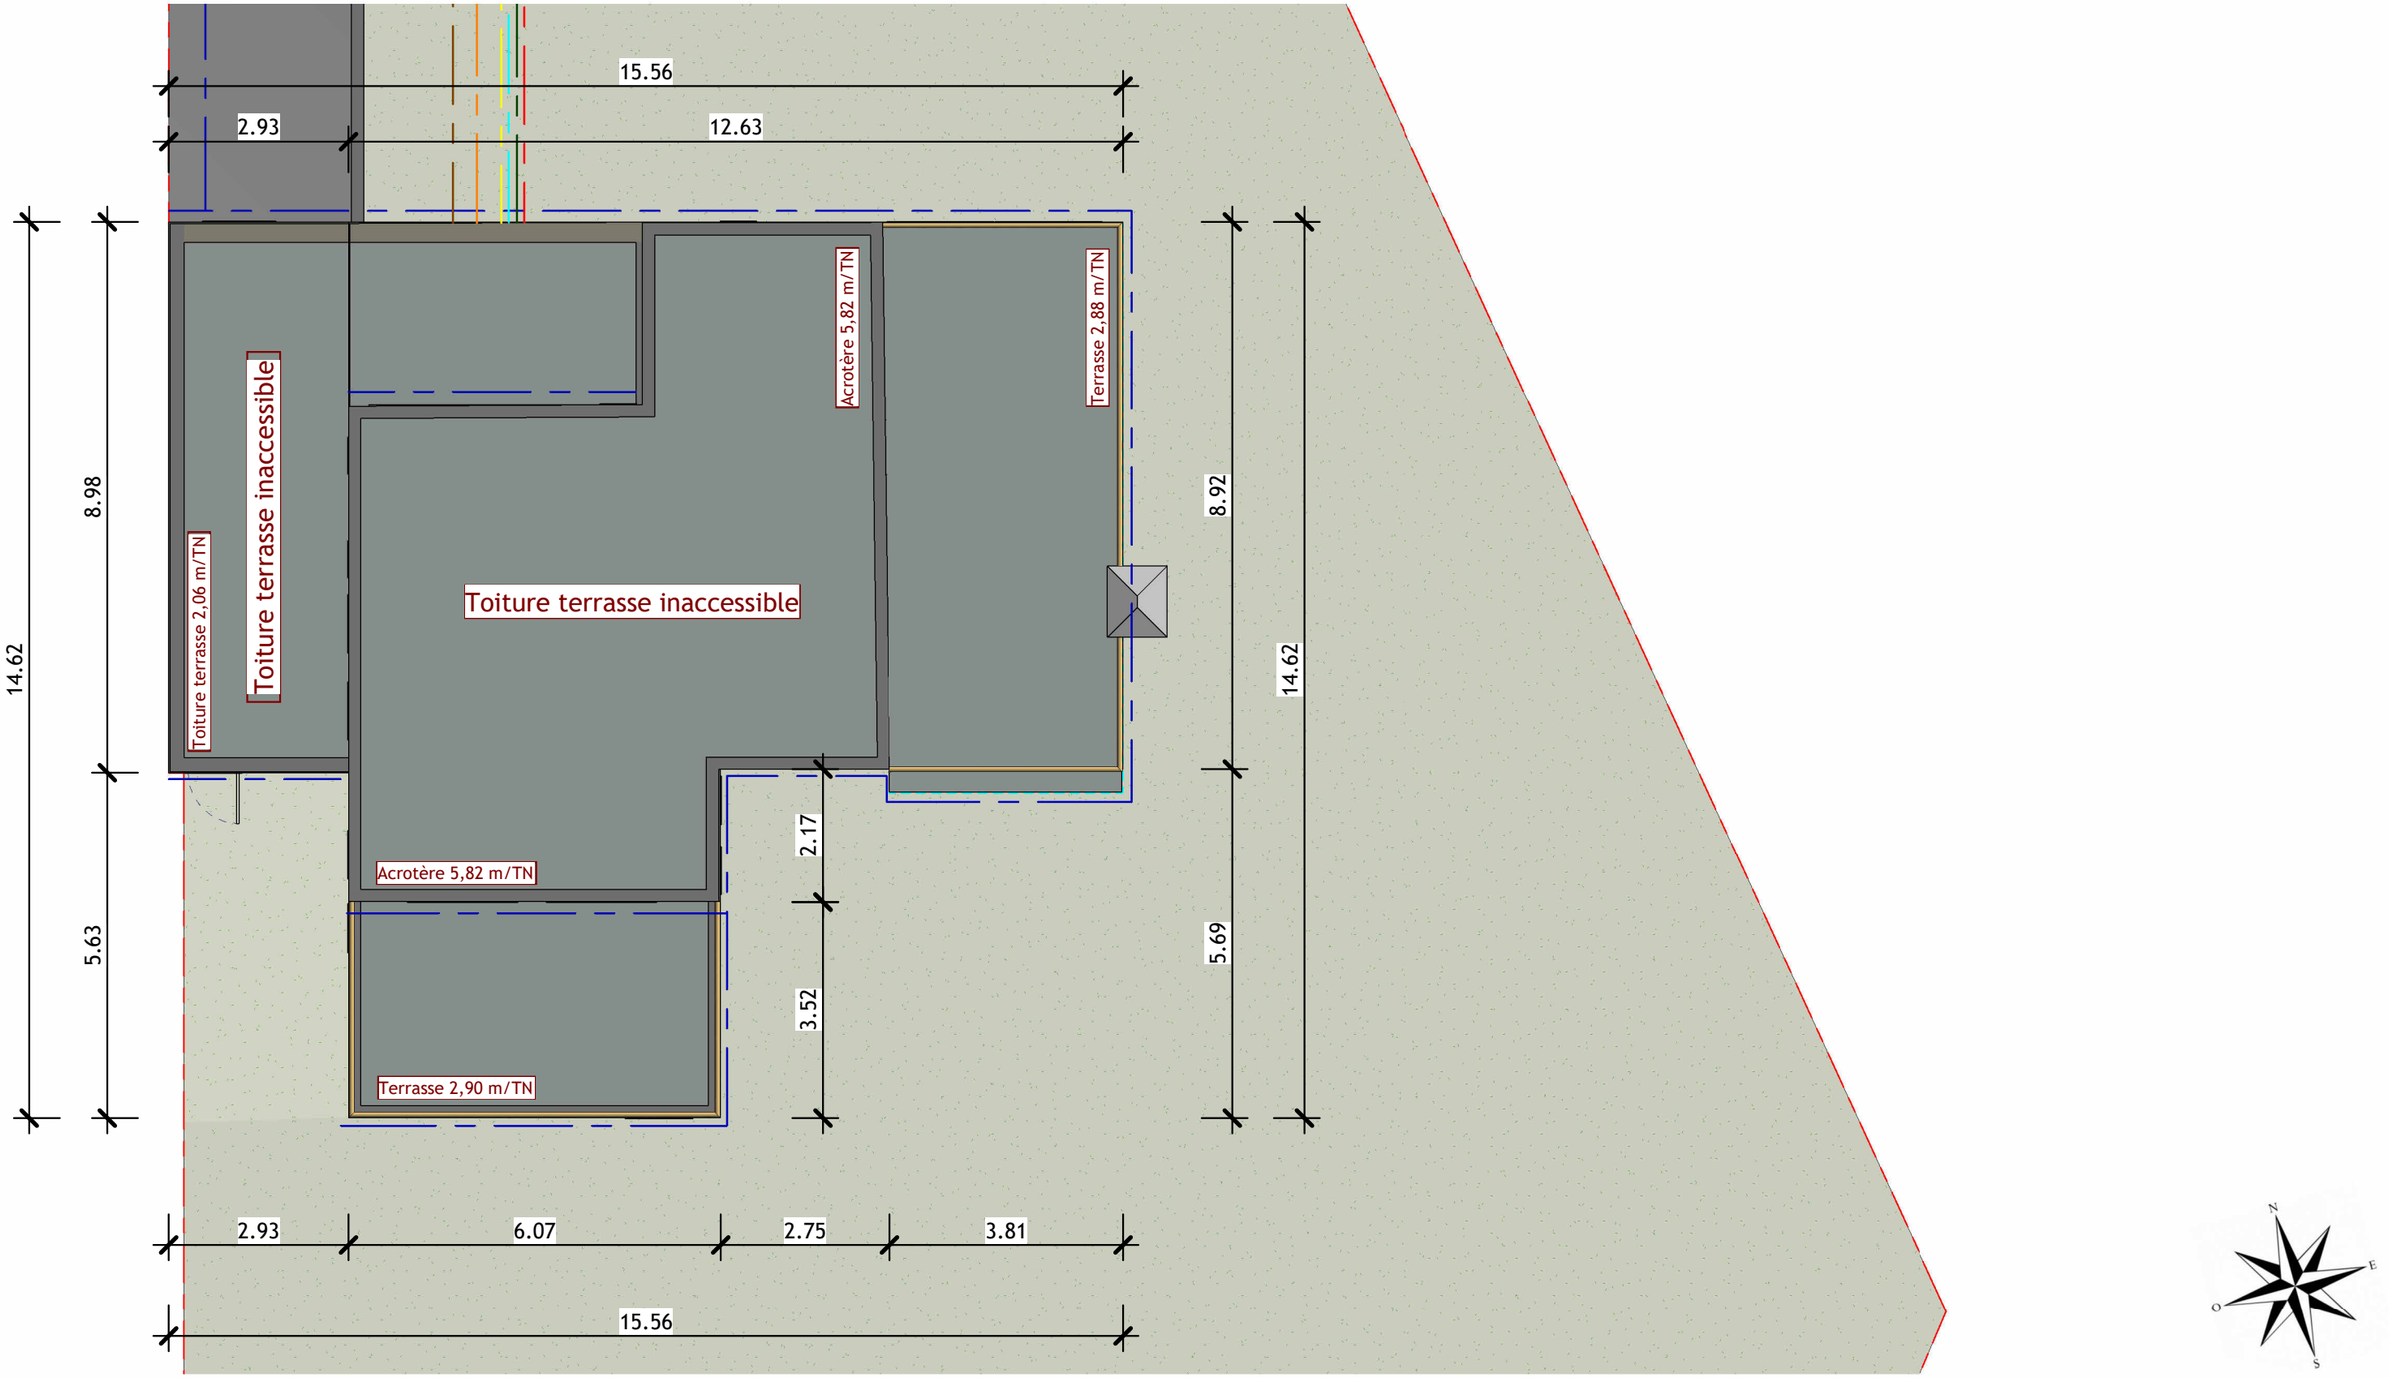

1 Plan de toitures - Etat projeté
Ech : 1 : 100

Bat_AFPA

FEDERATION COMPAGNONNIQUE

A.COLLIN

Ech : 1 : 100


05/03/2026

PERMIS DE CONSTRUIRE

PC 05-5

Plan de toiture - Etat projeté

Nomenclature des révisions		
N°INDICE	Date	Description

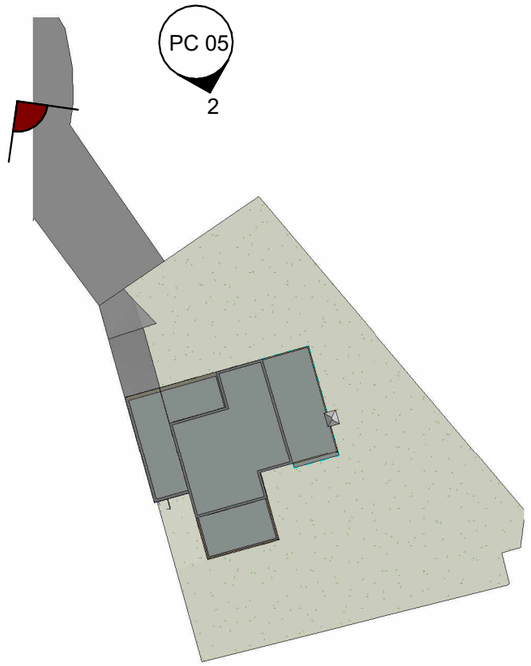

1 Plan Masse PC 06
Ech : 1 : 500







Bat_AFPA

FEDERATION COMPAGNONNIQUE

A.COLLIN

Ech : 1 : 500

05/03/2026


PERMIS DE CONSTRUIRE

PC 06

Insertion

Nomenclature des révisions

N°INDICE	Date	Description

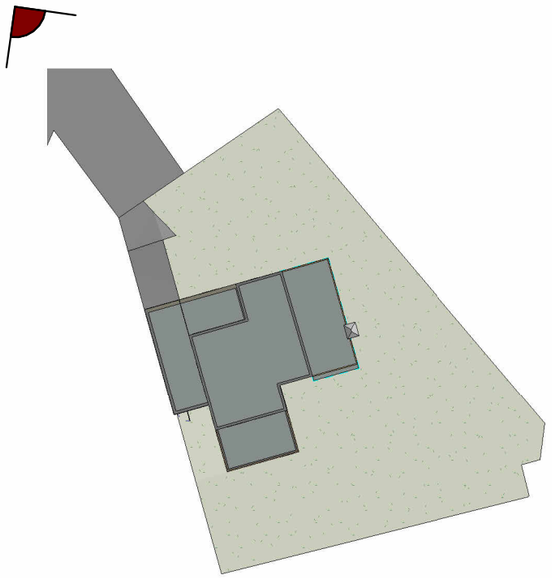

1 Plan Masse PC 07
Ech : 1 : 500



N
O E
S

Bat_AFPA

FEDERATION COMPAGNONNIQUE

A.COLLIN

Ech : 1 : 500

05/03/2026


PERMIS DE CONSTRUIRE

PC 07

Point de vue - Proche

Nomenclature des révisions

N°INDICE	Date	Description

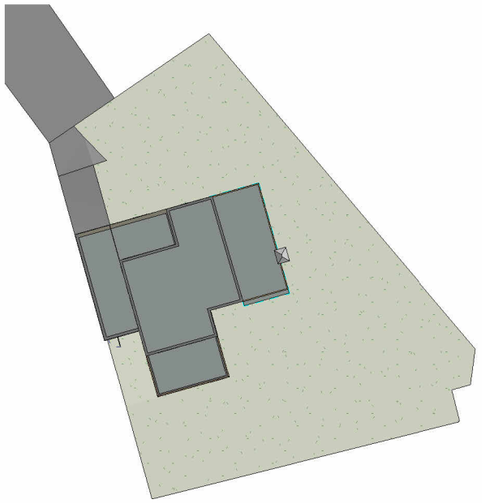

1 Plan Masse PC 08
Ech : 1 : 500





Bat_AFPA

FEDERATION COMPAGNONNIQUE

A.COLLIN

Ech : 1 : 500

Nomenclature des révisions		
N°INDICE	Date	Description

05/03/2026

PERMIS DE CONSTRUIRE

PC 08

Point de vue - Lointain

Bat_AFPA

FEDERATION COMPAGNONNIQUE

A.COLLIN

Ech :

05/03/2026


PERMIS DE CONSTRUIRE

PC 39/40


Plan de niveaux - RDC

Nomenclature des révisions

N°INDICE	Date	Description

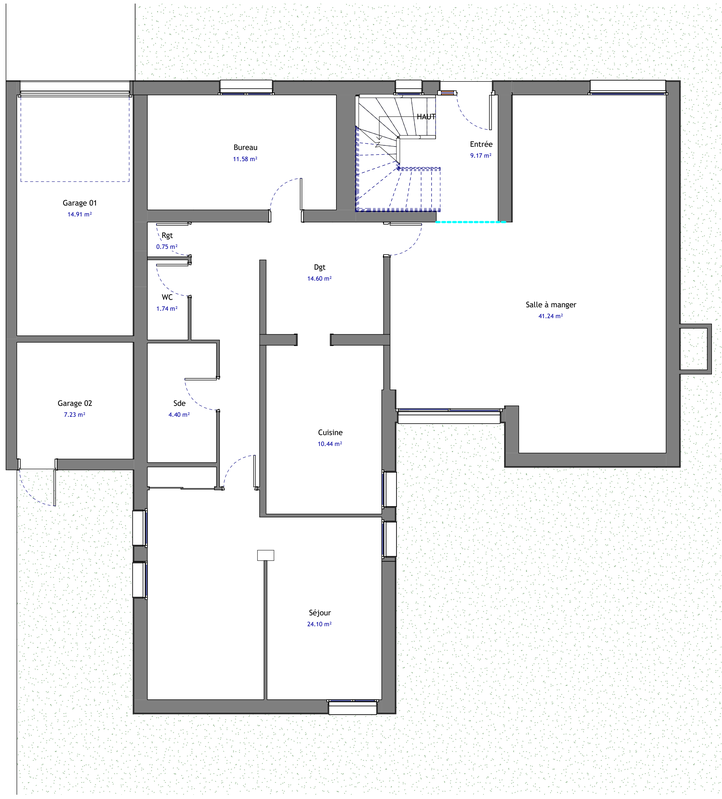

1 EXIST - RDC
Ech : 1 : 50

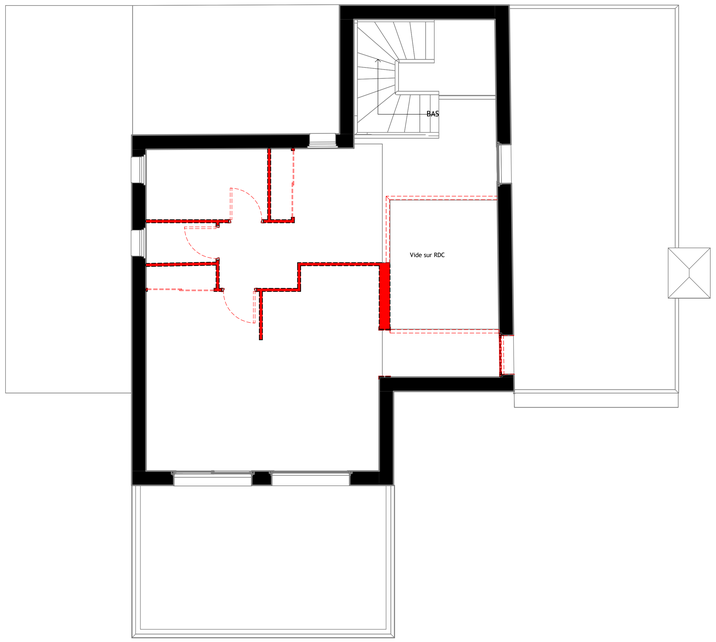


2 DEMOL - R+1
Ech : 1 : 50



5 Rendu 1
Ech : 1 : 1


Nomenclature des pièces		
Niveau	Nom	Surface
RDC		
RDC	Entrée	9.17 m²
RDC	Bureau	11.58 m²
RDC	Garage 01	14.91 m²
RDC	Garage 02	7.23 m²
RDC	Sde	4.40 m²
RDC	Cuisine	10.44 m²
RDC	Dgt	14.60 m²
RDC	Séjour	24.10 m²
RDC	WC	1.74 m²
RDC	Rgt	0.75 m²
RDC	Salle à manger	41.24 m²
RDC: 11		140.16 m²
R+1		
R+1	Dgt 02	13.70 m²
R+1	Sde 02	4.58 m²
R+1	WC 02	1.49 m²
R+1	Espace nuit	23.30 m²
R+1	Dgt 03	2.79 m²
R+1	Terrasse 01	35.36 m²
R+1	Terrasse 02	18.84 m²
R+1: 7		100.07 m²
Total général: 18		240.22 m²

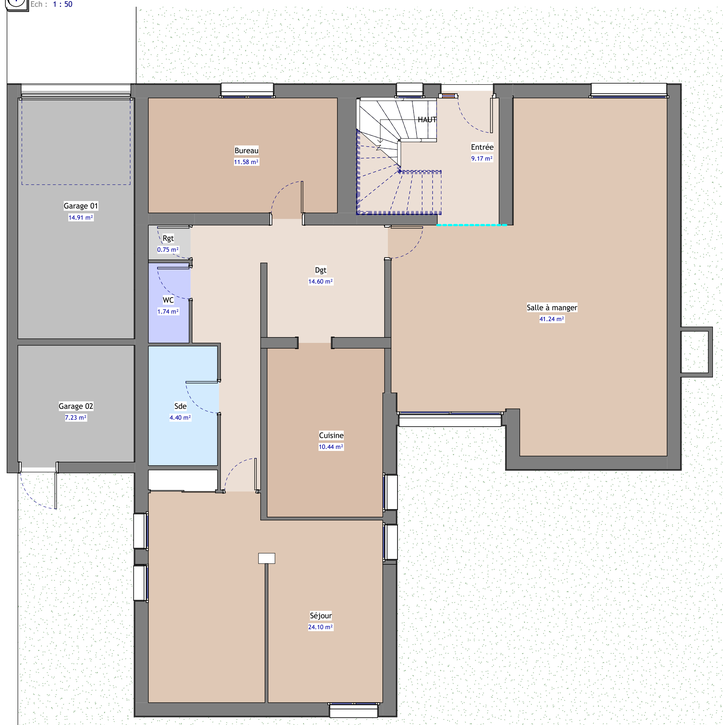

Coloriage par nom des pièces

- Bureau
- Cuisine
- Dgt
- Entrée
- Garage 01
- Garage 02
- Rgt
- Salle à manger
- Sde
- Séjour
- WC

4 RDC - Pièces
Ech : 1 : 50

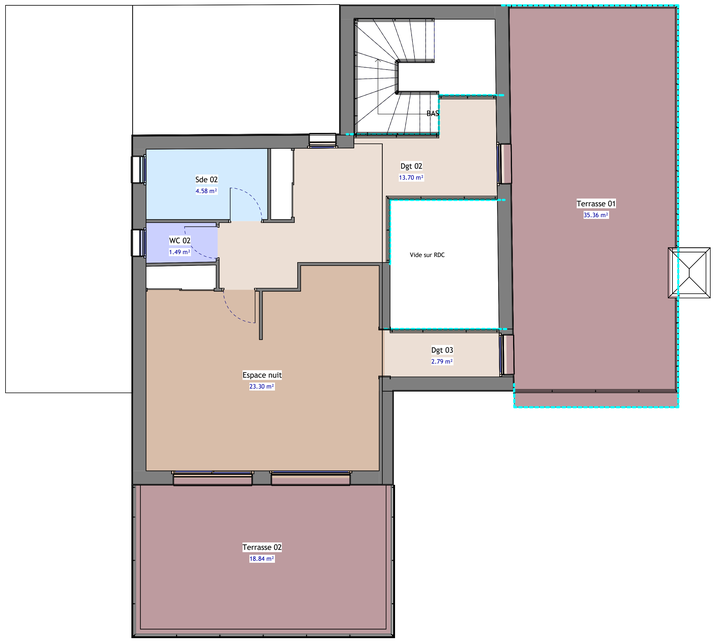

Coloriage par nom des pièces

- Dgt 02
- Dgt 03
- Espace nuit
- Sde 02
- Terrasse 01
- Terrasse 02
- WC 02

3 R+1 - Pièces
Ech : 1 : 50



6 Rendu 2
Ech : 1 : 1

Bat_AFPA		A.COLLIN	Nomenclature des révisions
FEDERATION COMPAGNONNIQUE		Ech. :Comme indiqué	N°INDICE / Date / Description
05/03/2026	Planche Plan de niveau RDC - R+1		
PERMIS DE CONSTRUIRE PC			